აბასთუმნის ისტორიული ნაწილის რეკონსტრუქცია
სახლი რუსთაველის ქ. № 70

KARKASI

აბასთუმნის ისტორიული ნაწილის რეკონსტრუქცია
სახლი რუსთაველის ქ. № 70

დირექტორი	გ. მაჭარაშვილი
არქიტექტორი	დ. კეჩხუაშვილი
შეასრულა	დ. კეჩხუაშვილი

შ.პ.ს. "კარკასი" ქ. თბილისი 2016წ.

№	ფურცლის დასახელება	ფურცელი
01	სატიტულო ფურცელი	არ-1
02	ნახაზების ჩამონათვალი და განმარტებითი ბარათი	არ-02
03	არსებული სიტუაციის ფოტოები	
04	ტოპო გეგმა	
05	პირველი სართულის გეგმა	
06	მეორე სართულის გეგმა	
07	სახურავის გეგმა	
08	ჭრილი-1	
09	ფასადი 1-5 ღერძებში	
10	ფასადი ა-დ ღერძებში	
11	ფასადი დ-ა ღერძებში	
12	ხის ნაკეთობები	
13	კიბე-1	
14	სარინელი	
15	კარ ფანჯრები	

განმარტებითი ბარათი

დაბა აბასთუმანში, რუსთაველის ქ.№70 ში მდებარე საცხოვრებელი სახლი, წარმოადგენს ქვით ნაგებ შენობას მინაშენი ხის შემინული აივნებით, რომლებიც ჭვირული დეკორის თემატიკით არის მორთული. სახლი გეგმაში წარმოადგენს მართკუთხედებისგან შედგენილ კომპოზიციას, კედლები აგებულია უხეშად ნათალი ადგილობრივი ქვით, რომელზედაც ფრაგმენტულად შერჩენილია ნალესობა. შენობა ორსართულიანია სართულშუა და სახურავის გადახურვები შესრულებულია ხის კონსტრუქციებით. სახურავი დაფარულია თუნუქის ძლიერ დაზიანებული ბურვილით.

წინამდებარე პროექტი ითვალისწინებს შენობის გარე იერსახის აღდგენა-რეაბილიტაციას, რაც გამოიხატება მისი სამი ფასადის რესტავრაციაში და პირვანდელი იერსახის აღდგენაში 1-5 და ბ-დ ღერძების ფარგლებში. პროექტი ამ ეტაპზე არ ითვალისწინებს შენობის შიგა ინტერიერების რემონტს ან რაიმე სხვა სახის სამუშაოებს.

ნაგებობის ტექნიკური მდგომარეობა და ჩასატარებელი სამუშაოები;
კონსტრუქციული დასკვნის საფუძველზე შენობა ძირითადად კონსტრუქციულად მდგრადია. საძირკველი კარგ მდგომარეობაშია, კედლის ქვები დაძრულია ფრაგმენტულად "1-5" ღერძების ფასადზე ფანჯრის თავზე, იხ. არ-03. არსებული სიტუაციის ფოტო-9. შენობას გააჩნია, ცენტრალური შესასვლელი ხის კიბე-1 და ეზოში ჩასასვლელი ლითონის კიბე-2. ძეგლზე ჩასატარებელი სამუშაოები ითვალისწინებს;
ხის კიბე-1 ის დემონტაჟს და მის ნაცვლად ბაზალტით მოპირკეთებული ახალი ქვის კიბის მოწყობას იხ. არ-13. ლითონის კიბე-2 გაიწმინდოს შეკეთდეს და შეიღებოს.
შენობის მთელ პერიმეტრზე წყალამრიდი სარინელის მოწყობა, რუსთაველის ქუჩაზე გამავალი 1-5 ღერძების ფასადზე ცოკოლის მოპირკეთება ბაზალტის ფილებით, შენობის მთელ პერიმეტრზე 1-5 და ბ-დ ღერძების ფარგლებში ბაზალტის ცოკოლის და კარნიზის მოწყობა. არსებული კედლების დაზიანებული ფრაგმენტების გადაწყობა. კედლების ნარჩენი ნალესობისგან გაწმენდა და ღრიჭოების შევსება ქვიშა ცემენტის ხსნარით მ 200. ხის ნაკეთობების და დეკორის დაზიანებული ფრაგმენტების დემონტაჟი და მისი ახლით ჩანაცვლება. აივნების მოაჯირების და რიკულების შეცვლა აუტენტურის შესაბამისად. ფასადებზე გამომავალი კარების დემონტაჟი შეკეთება, რესტავრაცია და ხელახალი მონტაჟი. არსებული შუშაბანდების სრული დემონტაჟი და მისი ჩანაცვლება ახალი ფანჯრებით რომლებიც შეივსება მინაპაკეტებით. სახურავის დაზიანებული კონსტრუქციების შეკეთება და ჩანაცვლება. ქარხნულად დაფერილი თუნუქის ბურვილის მოწყობა. სამღებრო სამუშაოების ჩატარება.
ყველა ახალი ხის ელემენტის დეკორი დამზადდეს არსებულიდან გადაღებული შაბლონებით და თარგებით.

არსებული სიტუაციის ფოტოები

KARKASI	შ.პ.ს. კარკასი				
	ობიექტი	აბასთუმნის ისტორიული ნაწილის რეკონსტრუქცია სახლი რუსთაველის ქ. № 70			
	სტადია	მუშა პროექტი			
დირექტორი	გ. მაჭარაშვილი		არსებული სიტუაციის ფოტოები		
არქიტექტორი	დ. კეჩხუაშვილი			ფურცლ. რაოდენ.	15
შეასრულა	დ. კეჩხუაშვილი			ფურცელი	არ -03 2016

ტოპო გეგმა

მასშტაბი 1:500

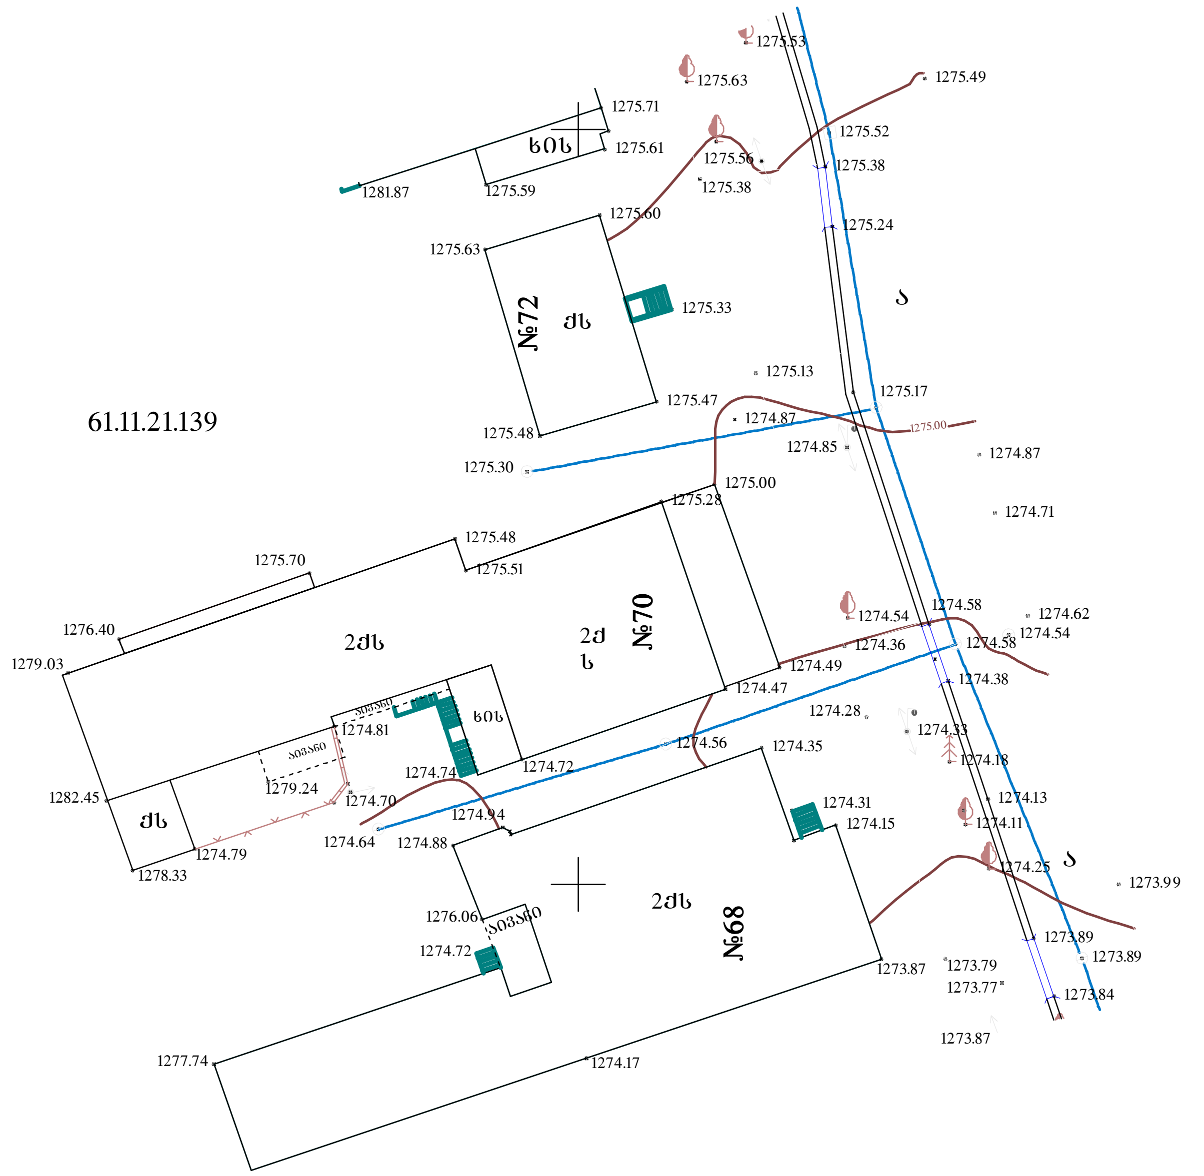

KARKASI	შ.პ.ს. კარკასი				
	ობიექტი	აბასთუმნის ისტორიული ნაწილის რეკონსტრუქცია სახლი რუსთაველის ქ. № 70			
	სტადია	ესკიზური პროექტი			
დირექტორი	გ. მაჭარაშვილი		ტოპო გეგმა		
არქიტექტორი	დ. კეჩხუაშვილი		მასშტაბი	ფურცლ. რაოდენ.	15
შეასრულა	დ. კეჩხუაშვილი			ფურცელი	არ -04 2016

პირველი სართულის გეგმა

მასშტაბი 1:200

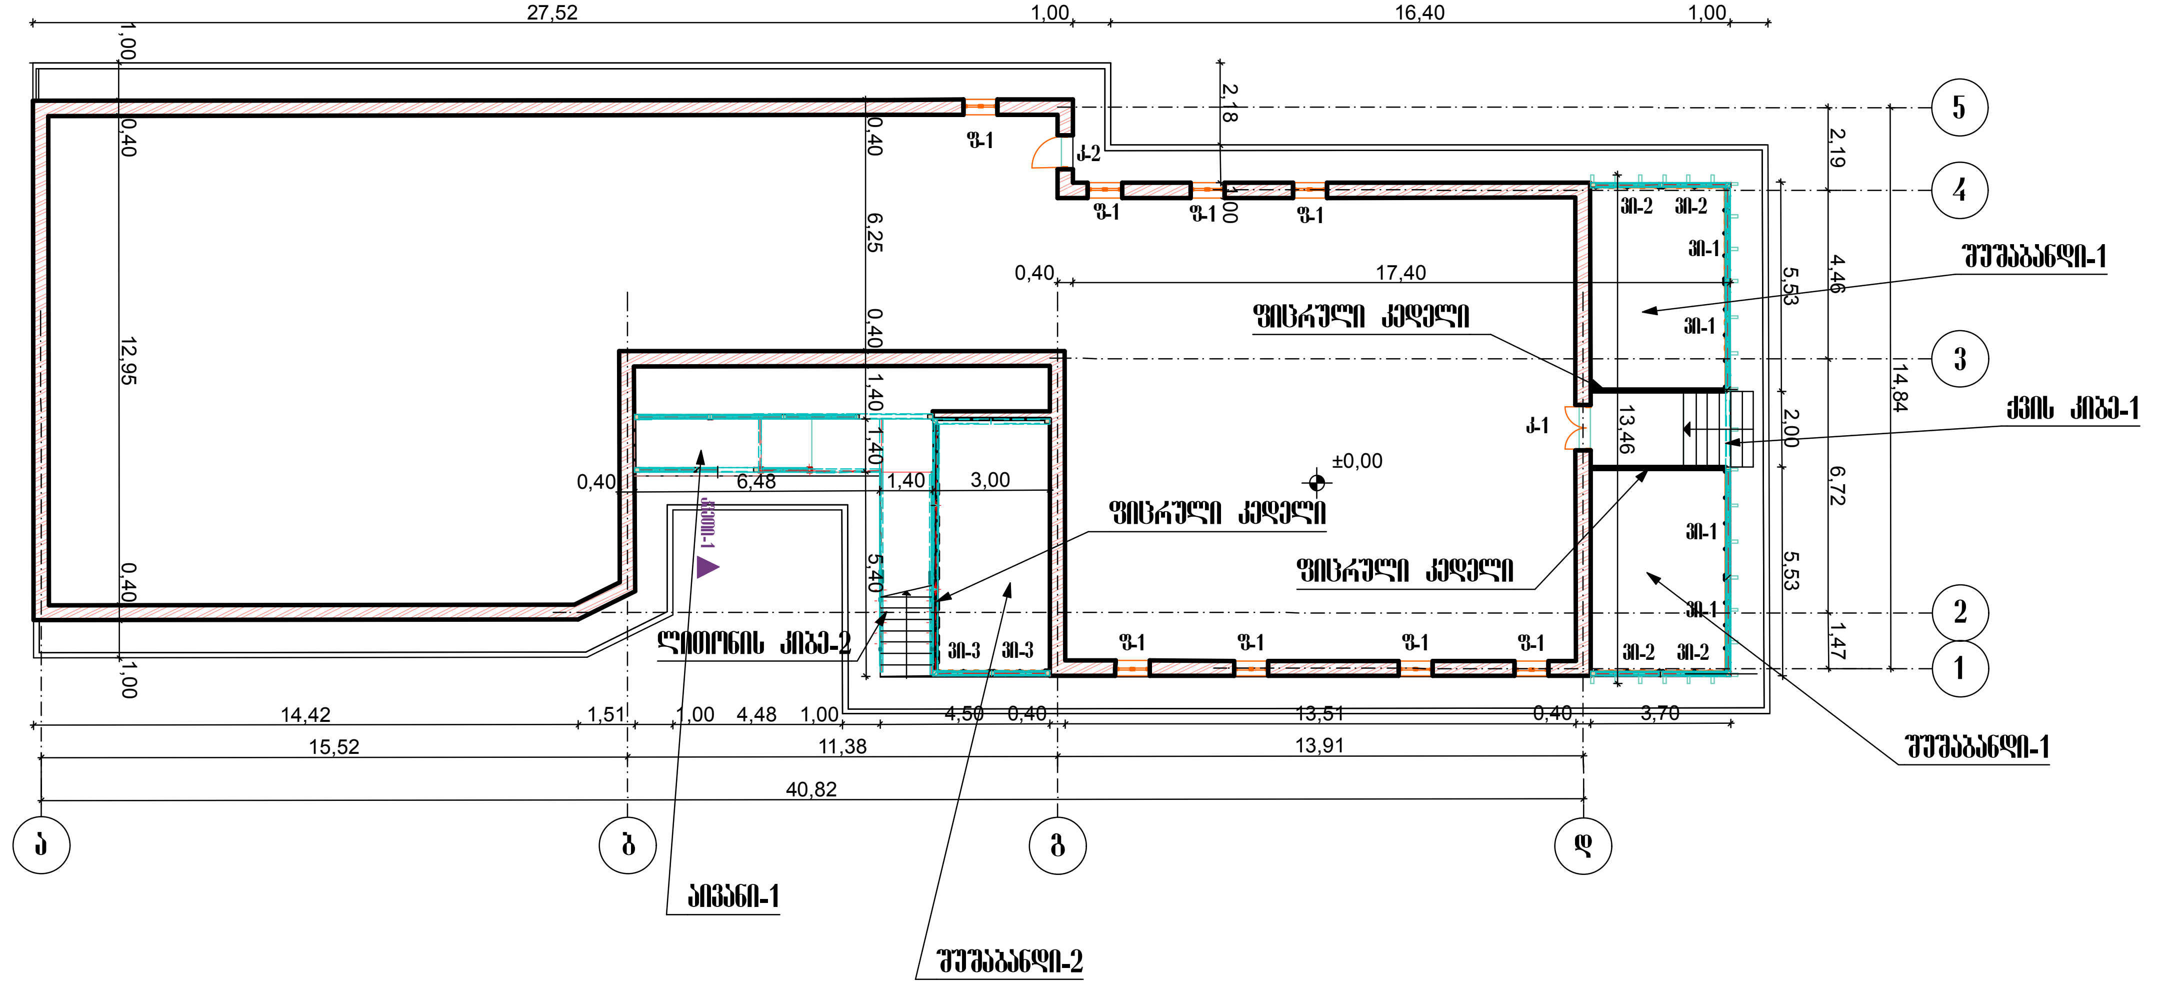

შენიშვნა

1. პროექტი ითვალისწინებს მხოლოდ შენობის ექსტერიერის სარეაბილიტაციო სამუშაოებს 1-5 და ბ-დ ღერძების ფარგლებში.

2. სარეაბილიტალიო სამუშაოები პროექტის ფარგლებში უტარდება შენობის ფასადებზე გამომავალ პირველი სართულის შუშაბანდი-1, შუშაბანდი-2 ს აივანი-1 ის წინა ფასადს და მეორე სართულის შუშაბანდი-3 ს და შუშაბანდი-4 ს და აივან-2 ს

3. შენობის ქვის კედლები იწმინდება, ჩაშლილი ნაწილები გადაეწყობა და ღრიჭოები შეივსება ქვიშა ცემენტის ხსნარით მ200 ფასადების ჯამური ფართის 35 %.

4. ფიცრული კედლები გაიწმინდოს დამუშავდეს და ორჯერადად შეიღების ახლიდან ქეთოვანი საღებავით ფერი შეთანხმდეს ავტორებთან, შესაღებში ჯამური ფართი - 48,00 მ²

KARKASI	შ.პ.ს. კარკასი				
	ობიექტი	აბასთუმნის ისტორიული ნაწილის რეკონსტრუქცია სახლი რუსთაველის ქ. № 70			
	სტადია	ესკიზური პროექტი			
დირექტორი	გ. მაჭარაშვილი		პირველი სართულის გეგმა		
არქიტექტორი	დ. კეჩხუაშვილი		მასშტაბი	ფურცლ. რაოდენ.	15
შეასრულა	დ. კეჩხუაშვილი			ფურცელი	არ -05 2016

მეორე სართულის გეგმა

მასშტაბი 1:200

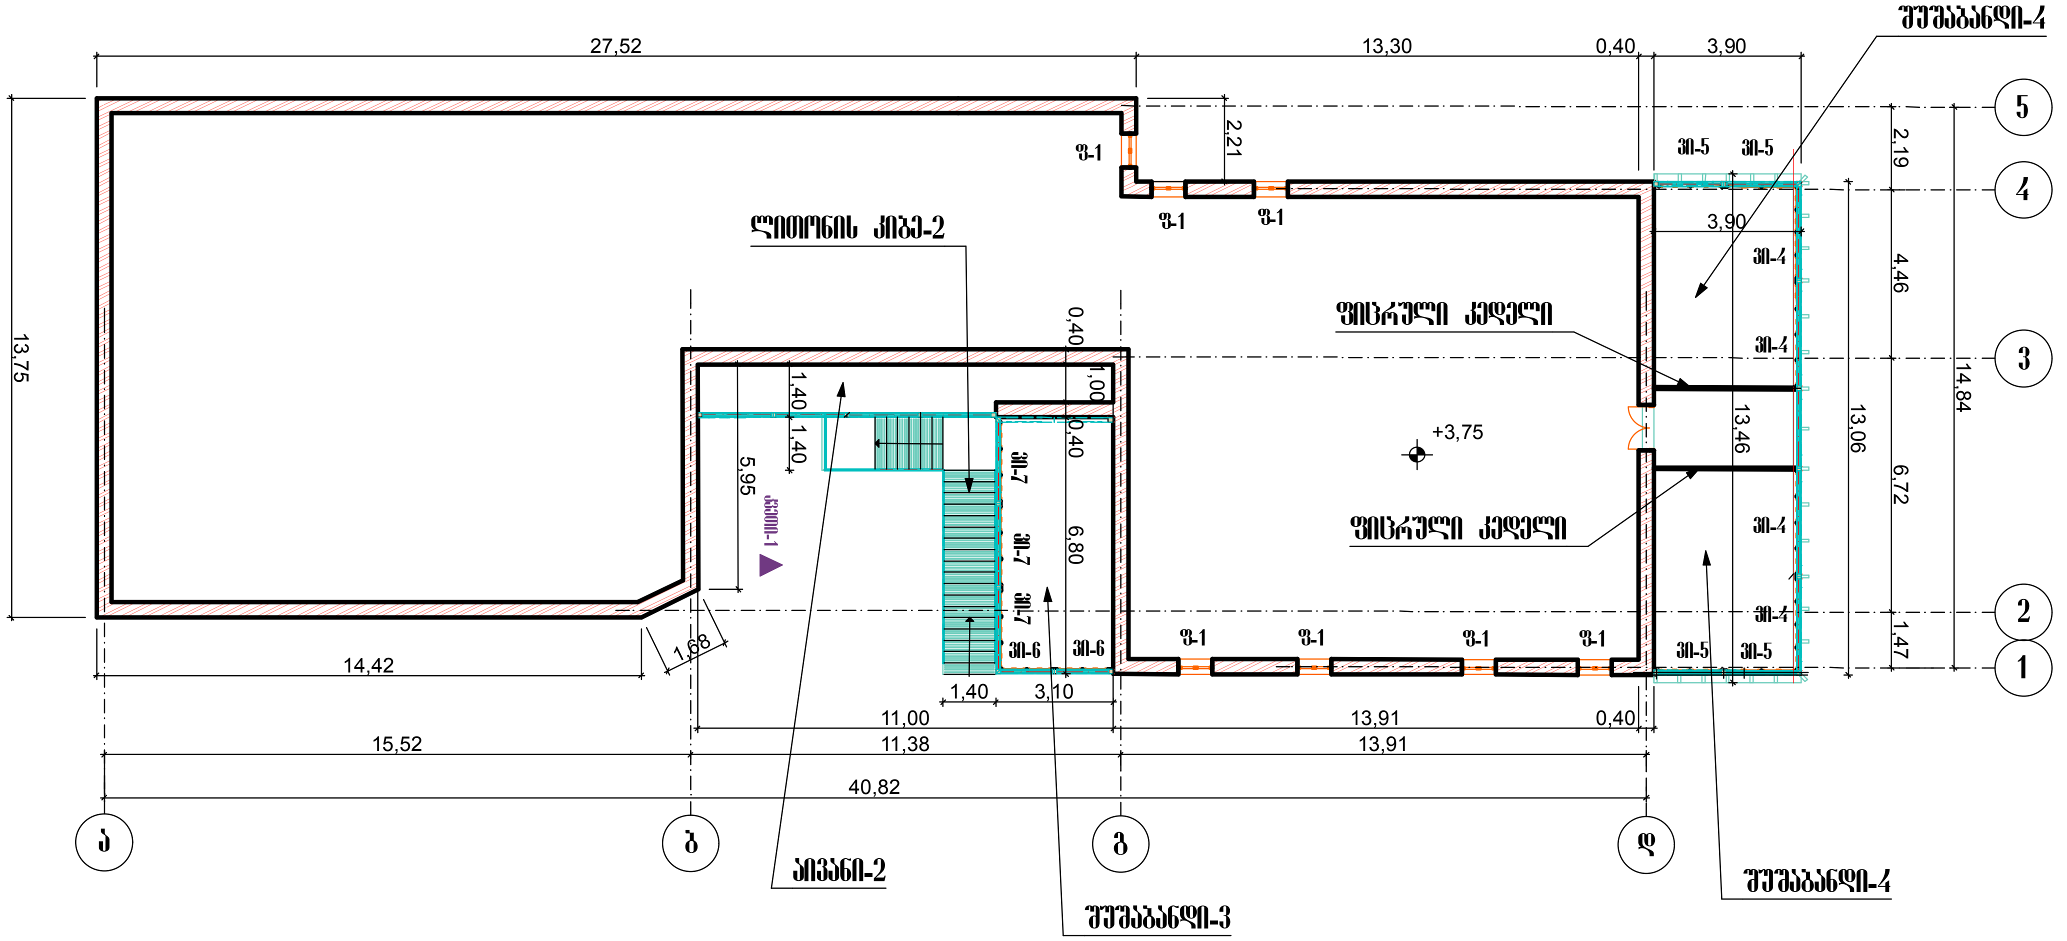

შენიშვნა

1. პროექტი ითვალისწინებს მხოლოდ შენობის ექსტერიერის სარეაბილიტაციო სამუშაოებს 1-5 და ბ-დ ღერძების ფარგლებში.
2. სარეაბილიტალიო სამუშაოები პროექტის ფარგლებში უტარდება შენობის ფასადებზე გამომავალ პირველი სართულის შუშაბანდი-1, შუშაბანდი-2 ს აივანი-1 ის წინა ფასადს და მეორე სართულის შუშაბანდი-3 ს და შუშაბანდი-4 ს და აივან-2 ს
3. შენობის ქვის კედლები იწმინდება, ჩაშლილი ნაწილები გადაეწყობა და ღრიჭოები შეივსება ქვიშა ცემენტის ხსნარით მ200 ფასადების ჯამური ფართის 35 %.

KARKASI	შ.პ.ს. კარკასი				
	ობიექტი	აბასთუმნის ისტორიული ნაწილის რეკონსტრუქცია სახლი რუსთაველის ქ. № 70			
	სტადია	ესკიზური პროექტი			
დირექტორი	გ. მაჭარაშვილი		მეორე სართულის გეგმა		
არქიტექტორი	დ. კეჩხუაშვილი		მასშტაბი	ფურცლ. რაოდენ.	15
შეასრულა	დ. კეჩხუაშვილი			ფურცელი	არ -06 2016

სახურავის გეგმა

მასშტაბი 1:200

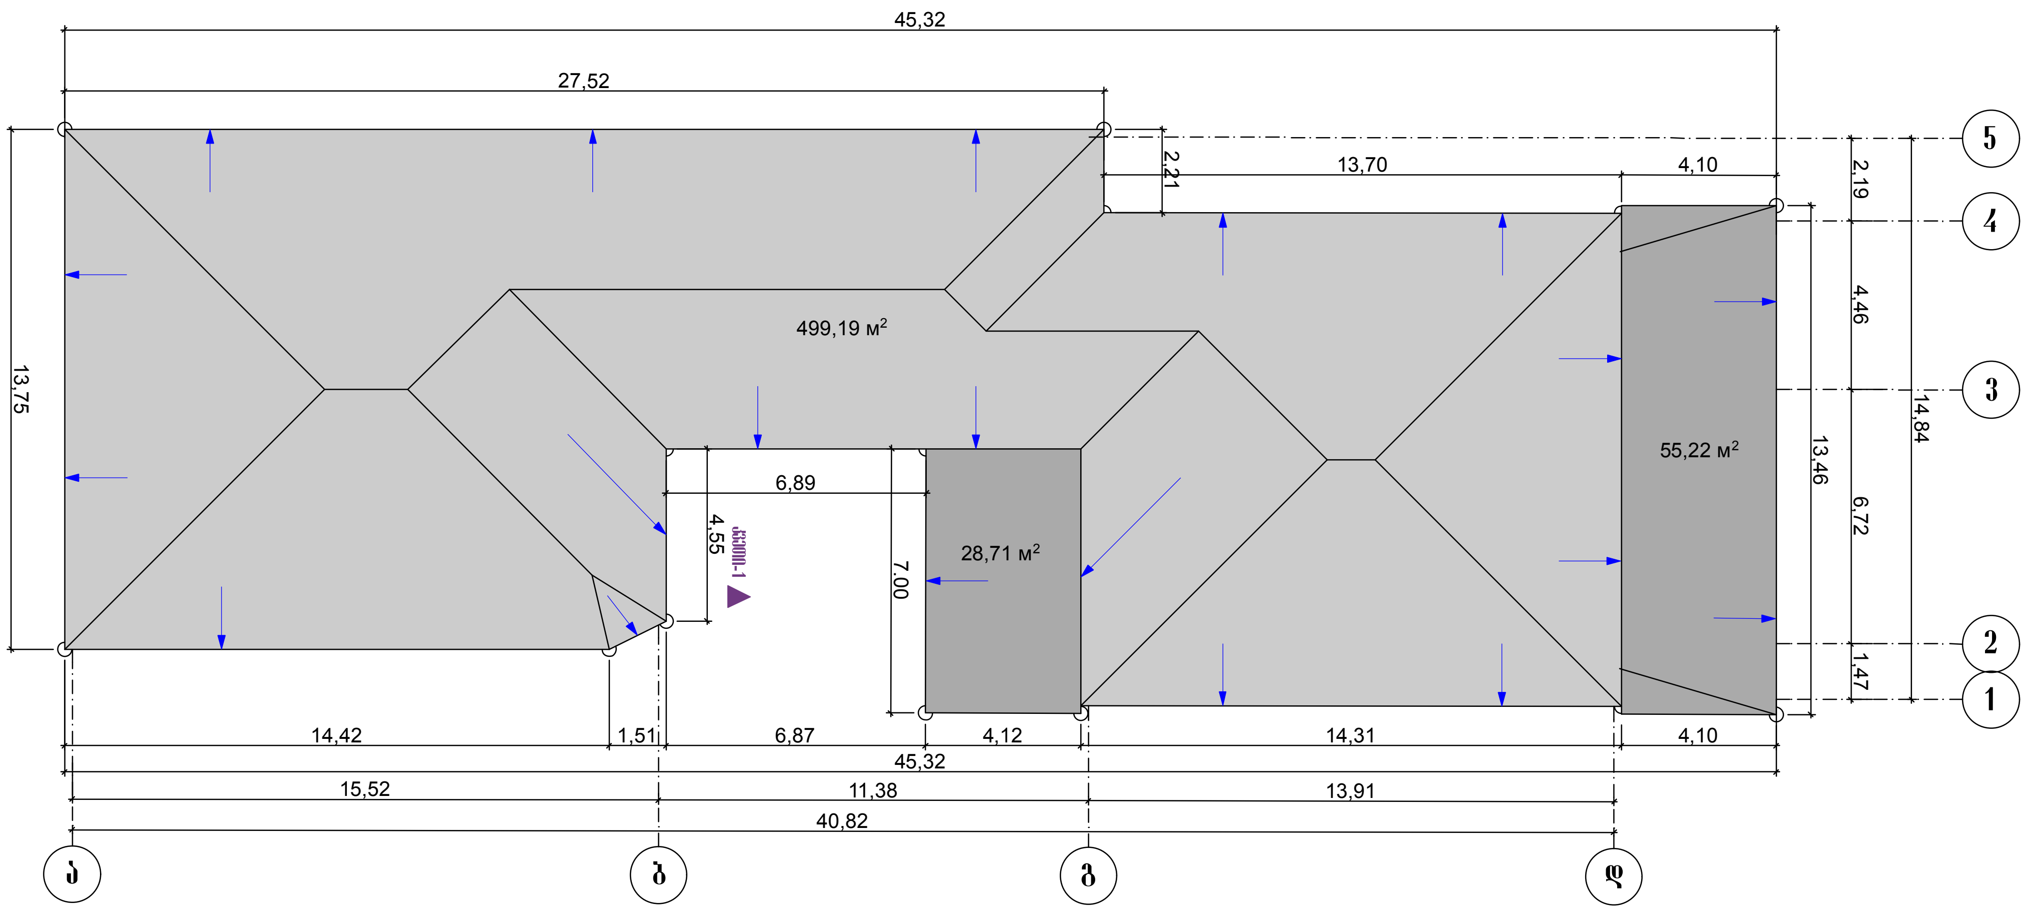

სახურავის მოწყობის სპეციფიკაცია				
№	დასახელება	რაოდ.ც.	მ²	გრძ./მ
1	სახურავის საფარის მოწყობა	3	758,10	—
2	შემკრები ღარი	14	—	131,61
3	ძაბრი	14	—	—
4	წყლის ჩამშვები მილი Ø 120 მმ.	14	—	99,40
5	მოფიცვრა 3 სმ	8,00 მ³	265,3	—

შენიშვნა

1. შენობის ამორტიზებული თუნუქის სახურავები მთლიანად იცვლება. ქარხნულად დაფერილი რუხი ფერის თუნუქის საფარით.
2. ასევე იცვლება მოფიცვრა, ხოლო ხის კონსტრუქცია შეკეთეს ფრაგმენტულად მთელი ფართის 35%.

KARKASI	შ.პ.ს. კარკასი				
	ობიექტი	აბასთუმნის ისტორიული ნაწილის რეკონსტრუქცია სახლი რუსთაველის ქ. № 70			
	სტადია	ესკიზური პროექტი			
დირექტორი	გ. მაჭარაშვილი		სახურავის გეგმა		
არქიტექტორი	დ. კეჩხუაშვილი		მასშტაბი	ფურცლ. რაოდენ.	15
შეასრულა	დ. კეჩხუაშვილი			ფურცელი	არ -07 2016

ფასადი ა–დ ღერძებში

მასშტაბი 1:200

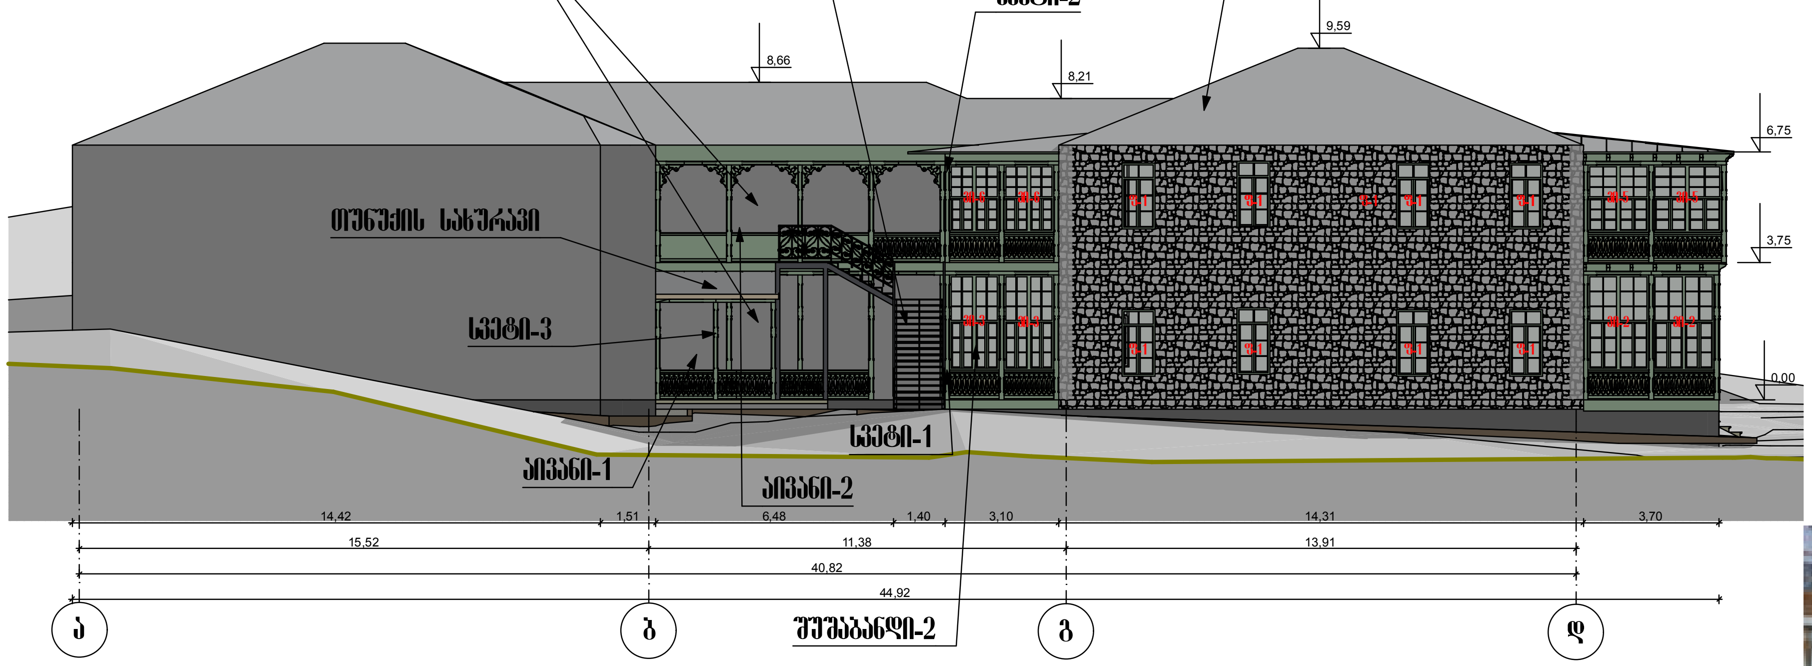

ლითონის კიბე გაიწმინდოს და შეიღებოს

მოაჯირის ავარიული შეფიცვრა შეიცვალოს ახლით. 24 მ²

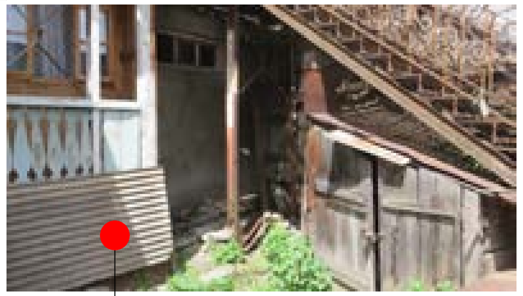

კიბის ქვეშ და მის მიმდებარე ტერიტორიაზე დაისხას ბეტონის ფილა 20მ².
დაზიანებული ლითონის სვეტი გამოიცვალოს და ჩაჯდეს ბეტონის საფუძველში. ლითონის ნაკეთობების დაზიანებული ნაწილები აღდგეს და გაძლიერდეს

ფასადის მოსაპირკეთებელი სამუშაოები					
№	დასახელება	რაოდენობა	დემონტაჟის მოცულობა	ზომა	სამუშაოს მოცულობა
1	ბაზალტის კარნიზის მოწყობა	—	—	23,89 გრძ/მ	0,22 მ³
2	ცოკოლის ბაზალტით მოპირკეთება	—	—	23,89X0.45	10,75 მ²
3	ქვიშა ცემენტის შევსების ხსნარი მ200	—	—	0,05X0,38X23,89	0,45 მ³
4	ნალესობისგან კედლების გასუფთავება	—	19,44 მ²	6.48X3	—
5	ლესვა-ღებვა	—	—	6.48X3	19,44 მ²
6	ჩაშლილი კედლის გადაწყობა	—	—	—	—
7	ქვის კედლების გაწმენდა ქვიშა ჭავლით	1	—	14,31X6,75	96,59 მ³
8	ქვის კედლების ღრიჭოების გამოლესვა ქვიშა ცემენტის ხსნარით მ200	1	—	14,31X6,75	4,85 მ³

შენიშვნა

1. პროექტი ითვალისწინებს მხოლოდ შენობის ექსტერიერის სარეაბილიტაციო სამუშაოებს 1-5 და ბ-დ ღერძების ფარგლებში.
2. სარეაბილიტალიო სამუშაოები პროექტის ფარგლებში უტარდება შენობის ფასადებზე გამომავალ პირველი სართულის შუშაბანდი-1, შუშაბანდი-2 ს აივანი-1 ის წინა ფასადს და მეორე სართულის შუშაბანდი-3 ს და შუშაბანდი-4 ს და აივან-2 ს.
3. შენობის ქვის კედლები იწმინდება, ჩაშლილი ნაწილები გადაეწყობა და ღრიჭოები შეივსება ქვიშა ცემენტის ხსნარით მ200 ფასადების ჯამური ფართის 5 %.
4. ფიცრული კედლები გაიწმინდოს დამუშავდეს და ორჯერადად შეიღების ახლიდან ზეთოვანი საღებავით ფერი შეთანხმდეს ავტორებთან, შესაღები ჯამური ფართი - 48,00 მ²

KARKASI	შ.პ.ს. კარკასი				
	ობიექტი	აბასთუმნის ისტორიული ნაწილის რეკონსტრუქცია სახლი რუსთაველის ქ. № 70			
	სტადია	ესკიზური პროექტი			
დირექტორი	გ. მაჭარაშვილი		ფასადი ა–დ ღერძებში		
არქიტექტორი	დ. კეჩხუაშვილი		მასშტაბი	ფურცლ. რაოდენ.	15
შეასრულა	დ. კეჩხუაშვილი			ფურცელი	არ -10 2016

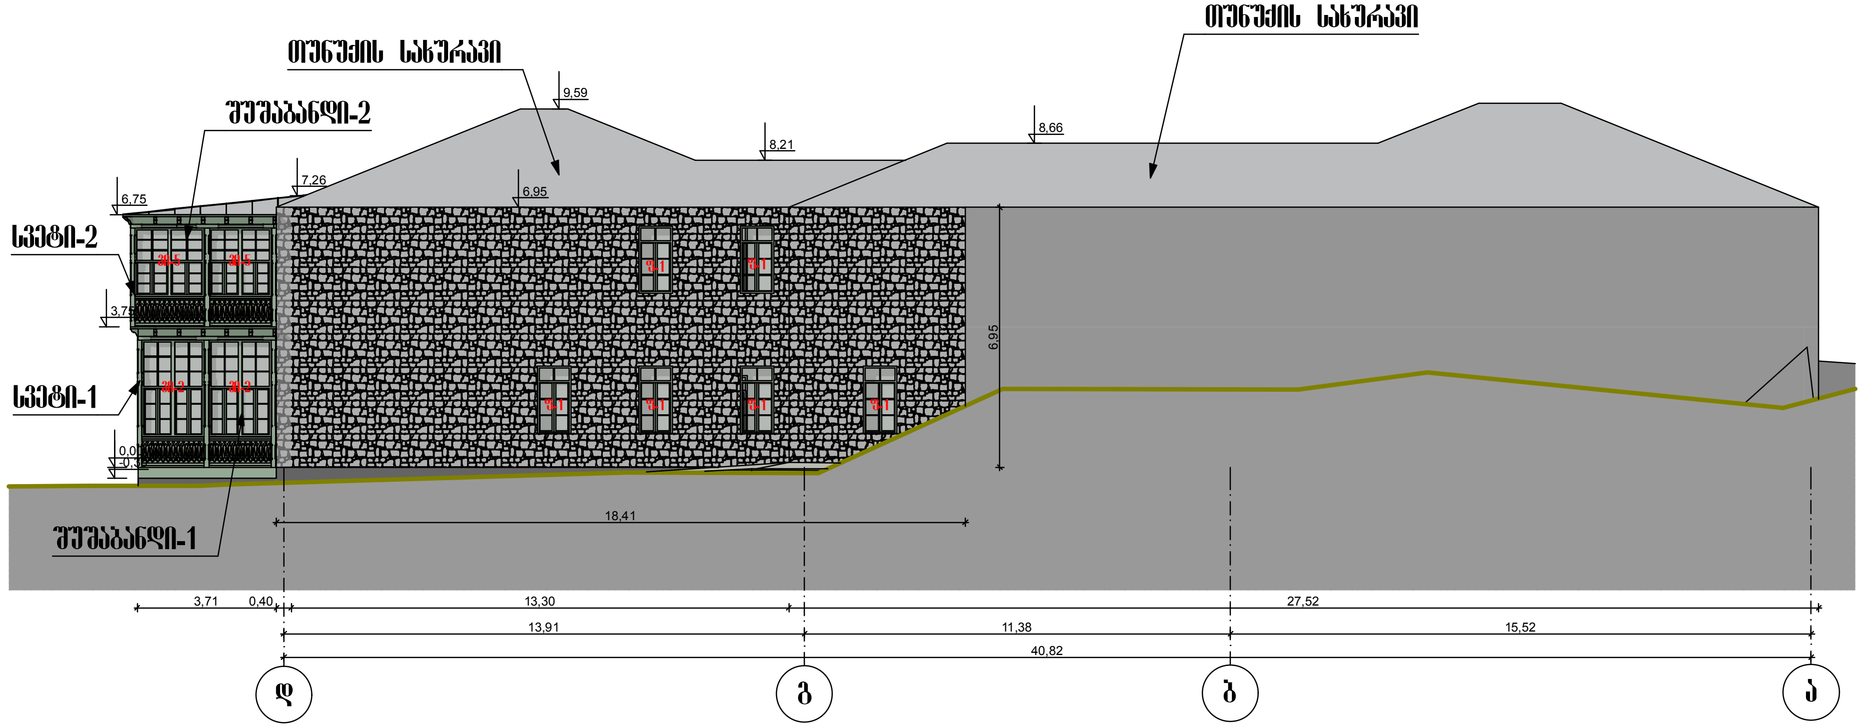

ფასადი დ–ა ღერძებში

მსაშტაბი 1:200

შენიშვნა

1. პროექტი ითვალისწინებს მხოლოდ შენობის ექსტერიერის სარეაბილიტაციო სამუშაოებს 1-5 და ბ-დ ღერძების ფარგლებში.
2. სარეაბილიტალიო სამუშაოები პროექტის ფარგლებში უტარდება შენობის ფასადებზე გამომავალ პირველი სართულის შუშაბანდი-1, შუშაბანდი-2 ს აივანი-1 ის წინა ფასადს და მეორე სართულის შუშაბანდი-3 ს და შუშაბანდი-4 ს და აივან-2 ს.
3. შენობის ქვის კედლები იწმინდება, ჩაშლილი ნაწილები გადაეწყობა და ღრიჭოები შეივსება ქვიშა ცემენტის ხსნარით მ200 ფასადების ჯამური ფართის 5 %.
4. ფიცრული კედლები გაიწმინდოს დამუშავდეს და ორჯერადად შეიღებს ახლიდან ზეთოვანი საღებავით ფერი შეთანხმდეს ავტორებთან, შესაღეფი ჯამური ფართი - 48,00 მ²

ფასადის მოსაპირკეთებელი სამუშაოები					
№	დასახელება	რაოდენობა	დემონტაჟის მოცულობა	ზომა	სამუშაოს მოცულობა
1	ბაზალტის კარნიზის მოწყობა	—	—	22,12 გრძ/მ	0,20 მ³
2	ცოკილის ბაზალტით მოპირკეთება	—	—	22.12X0.45	9,95 მ²
3	ქვიშა ცემენტის შევსების ხსნარი მ200	—	—	0,05X0,38X22,12	0,42 მ³
4	ნალესობისგან კედლების გასუფთავება	—	153,73 მ²	22,12X6,95	—
5	ლესვა-ღებვა	—	—	—	—
6	ჩაშლილი კედლის გადაწყობა	—	—	—	—
7	ქვის კედლების გაწმენდა ქვიშა ჭავლით	1	—	22,12X6,95	153,73 მ²
8	ქვის კედლების ღრიჭოების გამოლესვა ქვიშა ცემენტის ხსნარით მ200	1	—	22,12X6,95	9,50 მ²

აღნიშნული კანალიზაციის მილი გაუქმდეს, გაკეთდეს ახალი და დამონტაჟდეს კედელზე, რომელიც შემდეგ შეიფუთება იგივე თუნუქით რასაც გამოვიყენებთ სახურავისთვის

KARKASI	შ.პ.ს. კარკასი				
	ობიექტი	აბასთუმნის ისტორიული ნაწილის რეკონსტრუქცია სახლი რუსთაველის ქ. № 70			
	სტადია	ესკიზური პროექტი			
დირექტორი	გ. მაჭარაშვილი		ფასადი დ–ა ღერძებში		
არქიტექტორი	დ. კეჩხუაშვილი		მასშტაბი	ფურცლ. რაოდენ.	15
შეასრულა	დ. კეჩხუაშვილი			ფურცელი	არ -11 2016

კვეთი–1

მასშტაბი 1:100

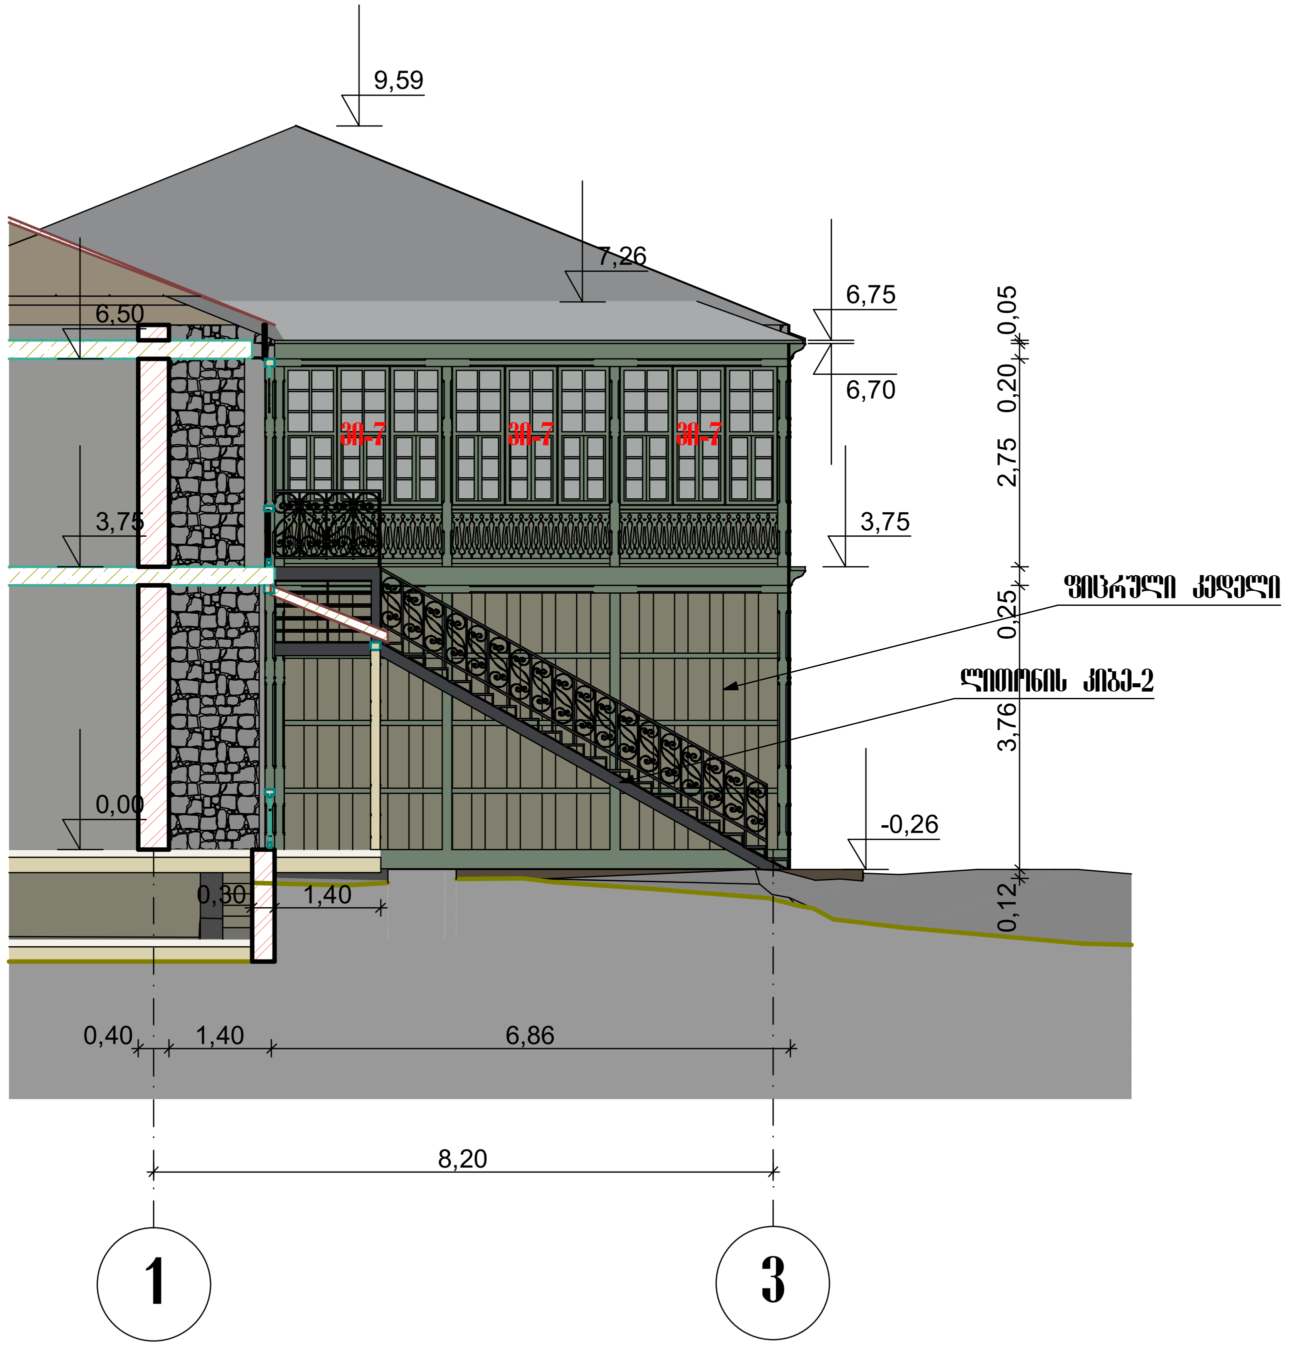

შენიშვნა

1. მოხდეს ვიტრაჟი-7 -ის დემონტაჟი და შეიცვალოს ახლით ის.-არ-15.
2. ლითონის კიბე-2, გაიწმინდოს, შეიცვალოსდაზიანებული დეტალები საერთო ფართის-25%. განხორციელდეს დაზიანებული დეტალების დადუღებას45 წერტილი. კიბე შიღებოს ორჯერადად ზეთოვანი საღებავით, ფერი შეთანხმდეს ავტორებთან.
3. ყველა ფიცრული კედელი გაიწმინდოს, დამუშავდეს და შიღებოს ორჯერადად ზეთოვანი საღებავით, ფერი შეთანხმდეს ავტორებთან. შესაღები საერთო ფართი - 48 მ²

KARKASI	შ.პ.ს. კარკასი				
	ობიექტი	აბასთუმნის ისტორიული ნაწილის რეკონსტრუქცია სახლი რუსთაველის ქ. № 70			
	სტადია	ესკიზური პროექტი			
დირექტორი	გ. მაჭარაშვილი		კვეთი–1		
არქიტექტორი	დ. კეჩხუაშვილი		მასშტაბი	ფურცლ. რაოდენ.	15
შეასრულა	დ. კეჩხუაშვილი			ფურცელი	არ -08 2016

ფასადი 1–5 ღერძებში

მასშტაბი 1:100, 1:20

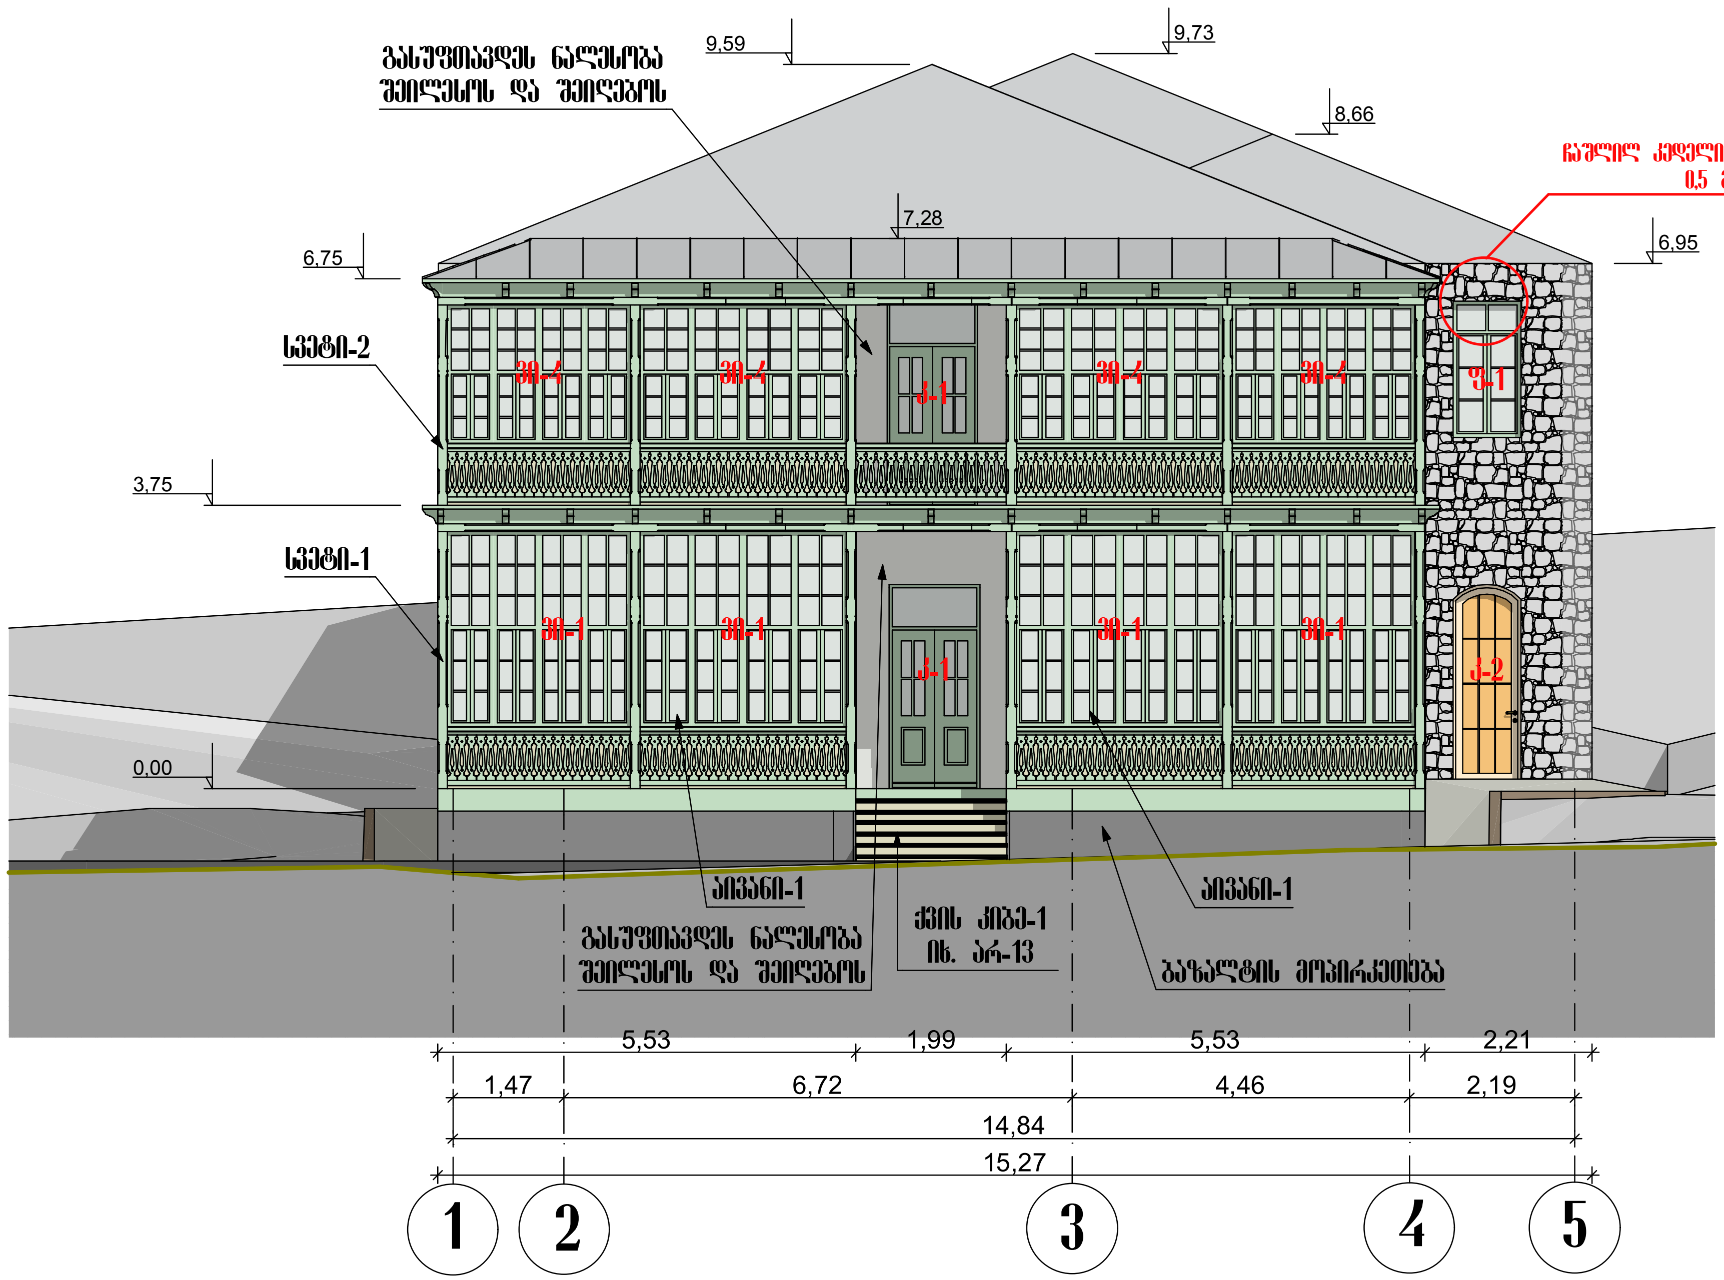

ბაზალტის მოპირკეთების კვეთი

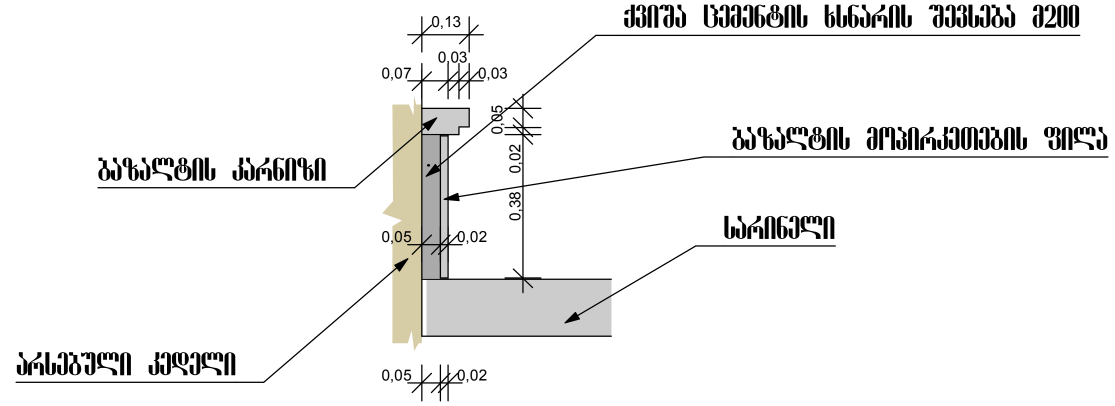

ფასადის მოსაპირკეთებელი სამუშაოები					
№	დასახელება	რაოდენობა	დემონტაჟის მოცულობა	ზომა	სამუშაოს მოცულობა
1	ბაზალტის კარნიზის მოწყობა	—	—	12,87 გრძ/მ	0,12 მ³
2	ცოკოლის ბაზალტით მოპირკეთება	—	—	12.87X0.45	5,80 მ²
3	ქვიშა ცემენტის შევსების ხსნარი მ200	—	—	0,05X0,38X12,87	0,25 მ³
4	ნალესობისგან კედლების გასუფთავება	—	13,43 მ²	1,99X6,75	—
5	ლესვა-ღებვა	—	—	1,99X6,75	13,43 მ²
6	ჩაშლილი კედლის გადაწყობა	—	0,5 მ³	—	0,5 მ³
7	ქვის კედლების გაწმენდა ქვიშა ჭავლით	1	—	2,21X6,95	15,36 მ³
8	ქვის კედლების ღრიჭოების ამოლესვა ქვიშა ცემენტის ხსნარით მ200	1	—	2,21X6,95	0,8 მ³

შენიშვნა

1. პროექტი ითვალისწინებს მხოლოდ შენობის ექსტერიერის სარეაბილიტაციო სამუშაოებს 1-5 და ბ-დ ღერძების ფარგლებში.
2. სარეაბილიტაციო სამუშაოები პროექტის ფარგლებში უტარდება შენობის ფასადებზე გამომავალ პირველი სართულის შუშაბანდი-1, შუშაბანდი-2 ს აივანი-1 ის წინა ფასადს და მეორე სართულის შუშაბანდი-3 ს და შუშაბანდი-4 ს და აივან-2 ს.
3. შენობის ქვის კედლები იწმინდება, ჩაშლილი ნაწილები გადაეწყობა და ღრიჭოები შეივსება ქვიშა ცემენტის ხსნარით მ200 ფასადების ჯამური ფართის 5 %.
4. ფიცრული კედლები გაიწმინდოს დამუშავდეს და ორჯერადად შეიღებოს ახლიდან ზეთოვანი საღებავით ფერი შეთანხმდეს ავტორებთან, შესაღები ჯამური ფართი - 48,00 მ²

KARKASI	შ.პ.ს. კარკასი				
	ობიექტი	აბასთუმნის ისტორიული ნაწილის რეკონსტრუქცია სახლი რუსთაველის ქ. № 70			
	სტადია	ესკიზური პროექტი			
დირექტორი	გ. მაჭარაშვილი		ფასადი 1–5 ღერძებში		
არქიტექტორი	დ. კეჩხუაშვილი		მასშტაბი	ფურცლ. რაოდენ.	15
შეასრულა	დ. კეჩხუაშვილი		ფურცელი	არ -09	2016

ხის ნაკეთობები

მასშტაბი 1:50

ხის ნაკეთობათა ნაკრები სპეციფიკაცია						
№	დასახელება	ნაკეთ. რაოდ. ც.	ზომები	ხის მასალის ხარჯი მ³ 1ცალზე	ჩასატარებელი სამუშაო	სულ ხის მასალის ხარჯი მ³
1	ხის სვეტი-1	22	0,13x0,13x3,40	0,06	გაიწმინდოს	—
2	ხის სვეტი-2	22	0,13x0,13x2,90	0,05	გაიწმინდოს	—
3	ხის სვეტი-3	3	0,13x0,13x2,65	0,05	შეიცვალოს ახლით	1,50
4	რიქულის დამჭერი ლარტყა-2	—	0,04x0,04x133,36	—	შეიცვალოს ახლით	0,21
5	ხის მოაჯირი	—	0,07x0,12x66,68	—	შეიცვალოს ახლით	0,56
6	გამკტავი კოჭი	—	0,13x0,1x66,68	—	გაიწმინდოს	0,87
7	შუბლის ფიცარი	—	0,25x0,04x47,76	—	შეიცვალოს ახლით	0,50
8	ხის ჭვირული რიქული	158	0,02x0,12x0,61	0,0015	შეიცვალოს ახლით	2,4
9	ხის ფარდა	8	0,60x0,60x0,02	0,004	შეიცვალოს ახლით	0,1
სულ ხის მასალის ხარჯი						6,14
შესაღები ფართი 406.23 მ²						

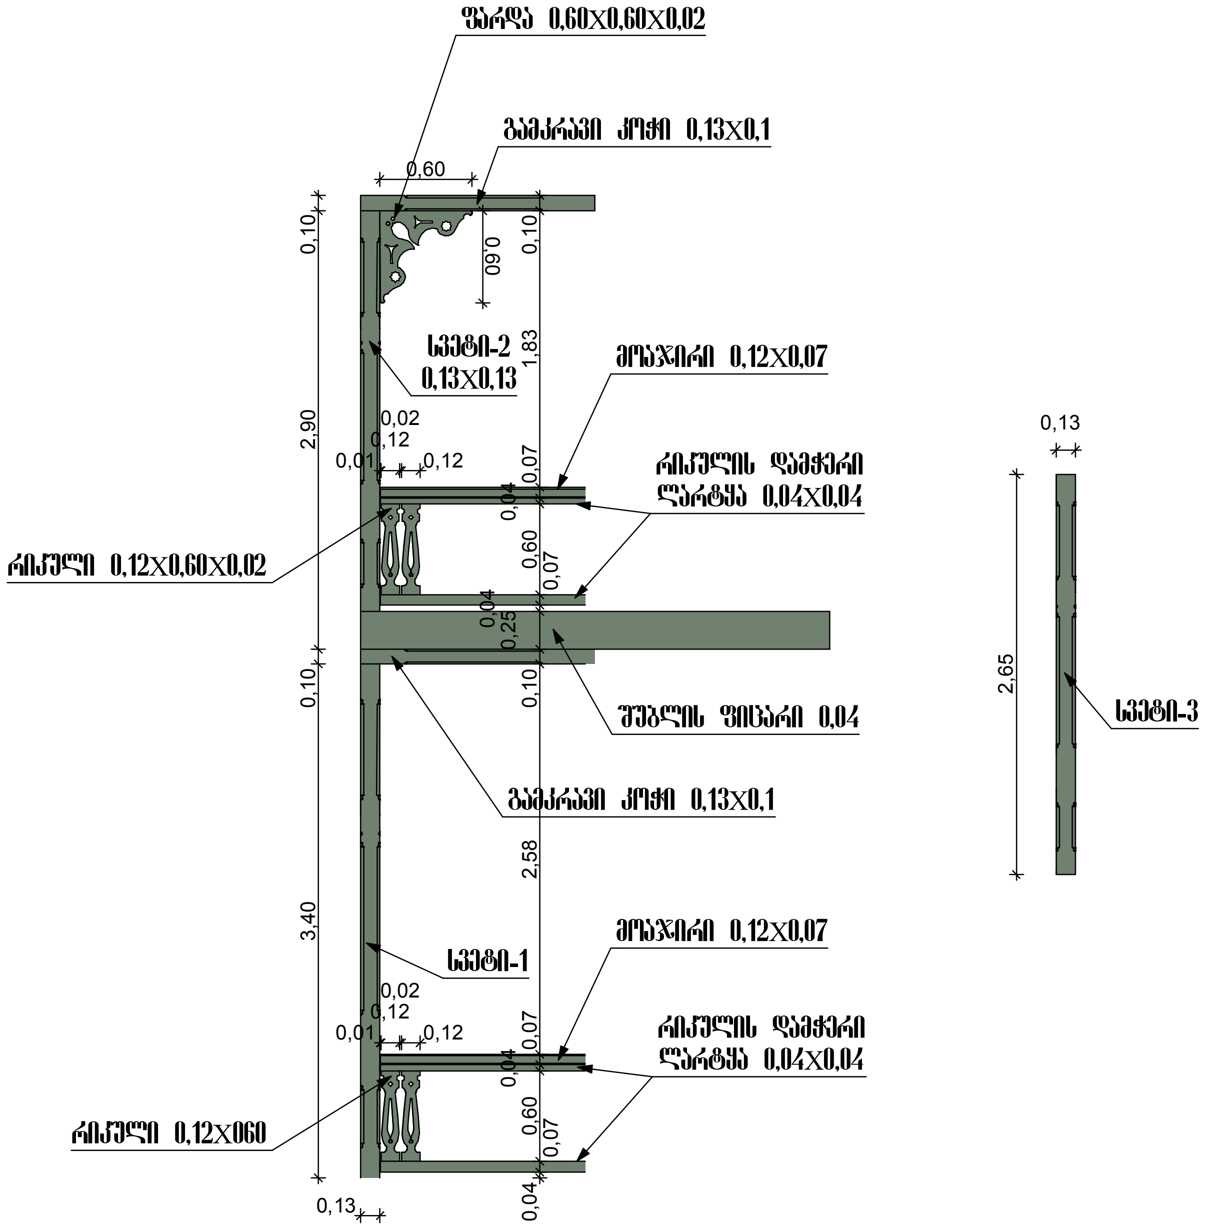

შენიშვნა

1. ამორტიზებული აივანი -1 იცვლება მთლიანად, იხ. ცხრილი და ფურც. არ-20
2. არსებული შუშაბანდი მოიხსნას და შეიცვალოს ახლით, იხ. ფურცელი არ-29
3. ხის ყველა დეტალი დამუშავდეს და შეიღებოს ორჯერადად ზეთოვანი საღებავით, ფერი შეთანხმდეს ავტორებთან.

KARKASI	შ.პ.ს. კარკასი				
	ობიექტი	აბასთუმნის ისტორიული ნაწილის რეკონსტრუქცია სახლი რუსთაველის ქ. № 70			
	სტადია	ესკიზური პროექტი			
დირექტორი	გ. მაჭარაშვილი		ხის ნაკეთობები		
არქიტექტორი	დ. კეჩხუაშვილი		მასშტაბი	ფურცლ. რაოდენ.	15
შეასრულა	დ. კეჩხუაშვილი			ფურცელი	არ -12 2016

კიბე-1

მასშტაბი 1:20

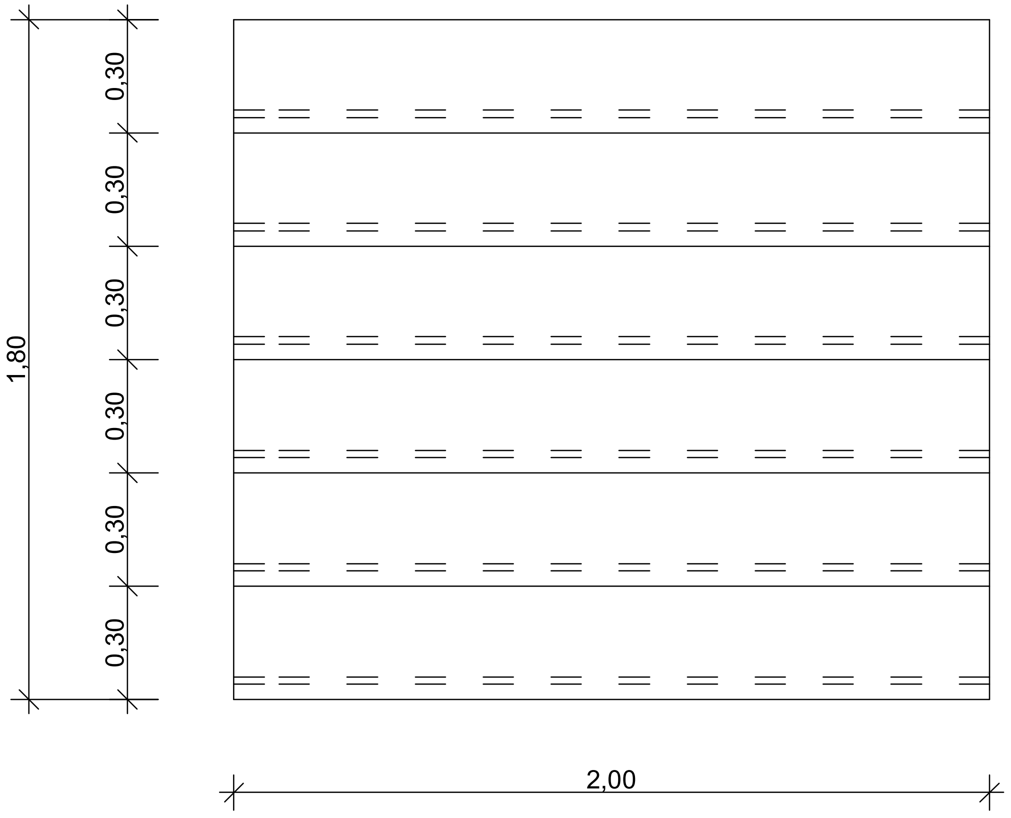

 

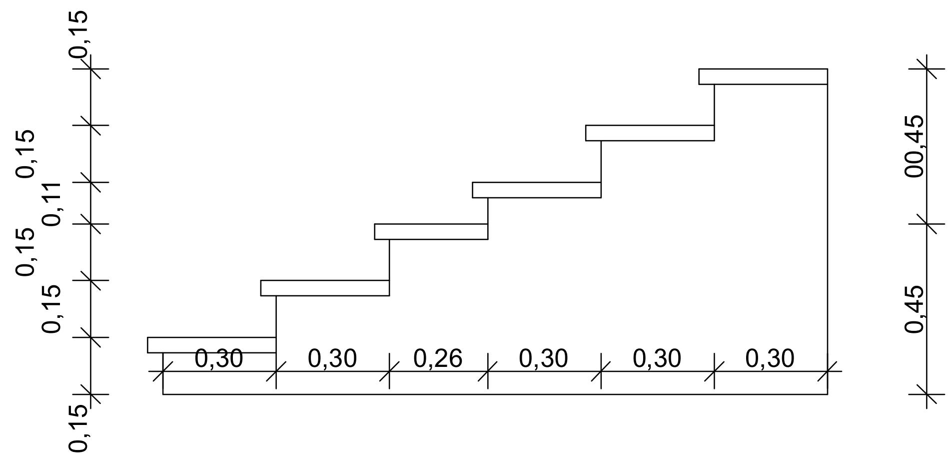

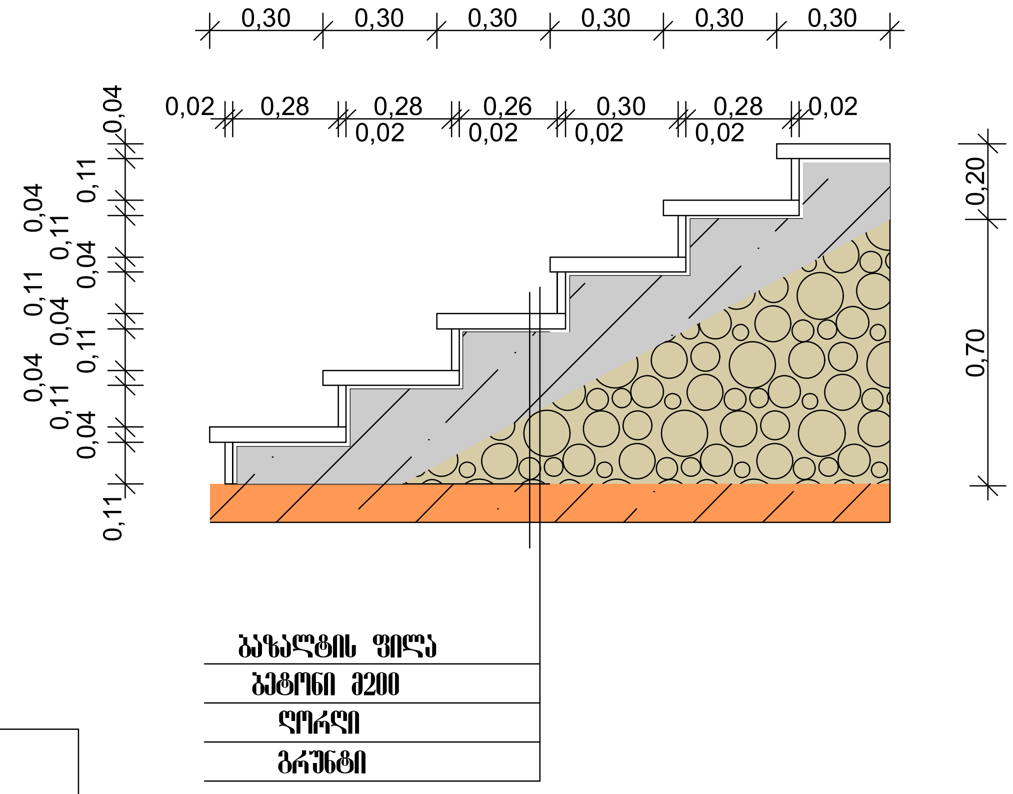

კიბე-1 და კიბე-2 მასალების სპეციფიკაცია

№	დასახელება	ზომები მ	მასალის ხარჯი $მ^3$
	კიბე-1		
1	ბაზალტის საფეხურის ფილა	2,00X1,80X0,04	0,14
2	ბაზალტის საფეხურის შუბლი	12,00X0,11X0,02	0,02
3	ბეტონი მ200	2,00X0,20	0,40
4	ღორღი	2,00X0,50	1,00

შენიშვნა

1. არსებული კიბე-1 დაიშალოს და მის ნაცვლად მოეწყოს ახალი ქვის კიბე წარმოდგენილი ახაზის შესაბამისად.

KARKASI	შ.პ.ს. კარკასი			
	ობიექტი	აბასთუმნის ისტორიული ნაწილის რეკონსტრუქცია სახლი რუსთაველის ქ. № 70		
	სტადია	ესკიზური პროექტი		
დირექტორი	გ. მაჭარაშვილი		კიბე–1	
არქიტექტორი	დ. კეჩხუაშვილი		მასშტაბი	ფურცლ. რაოდენ. 15
შეასრულა	დ. კეჩხუაშვილი			ფურცელი არ -13 2016

სარინელი

მასშტაბი 1:200, 1:20

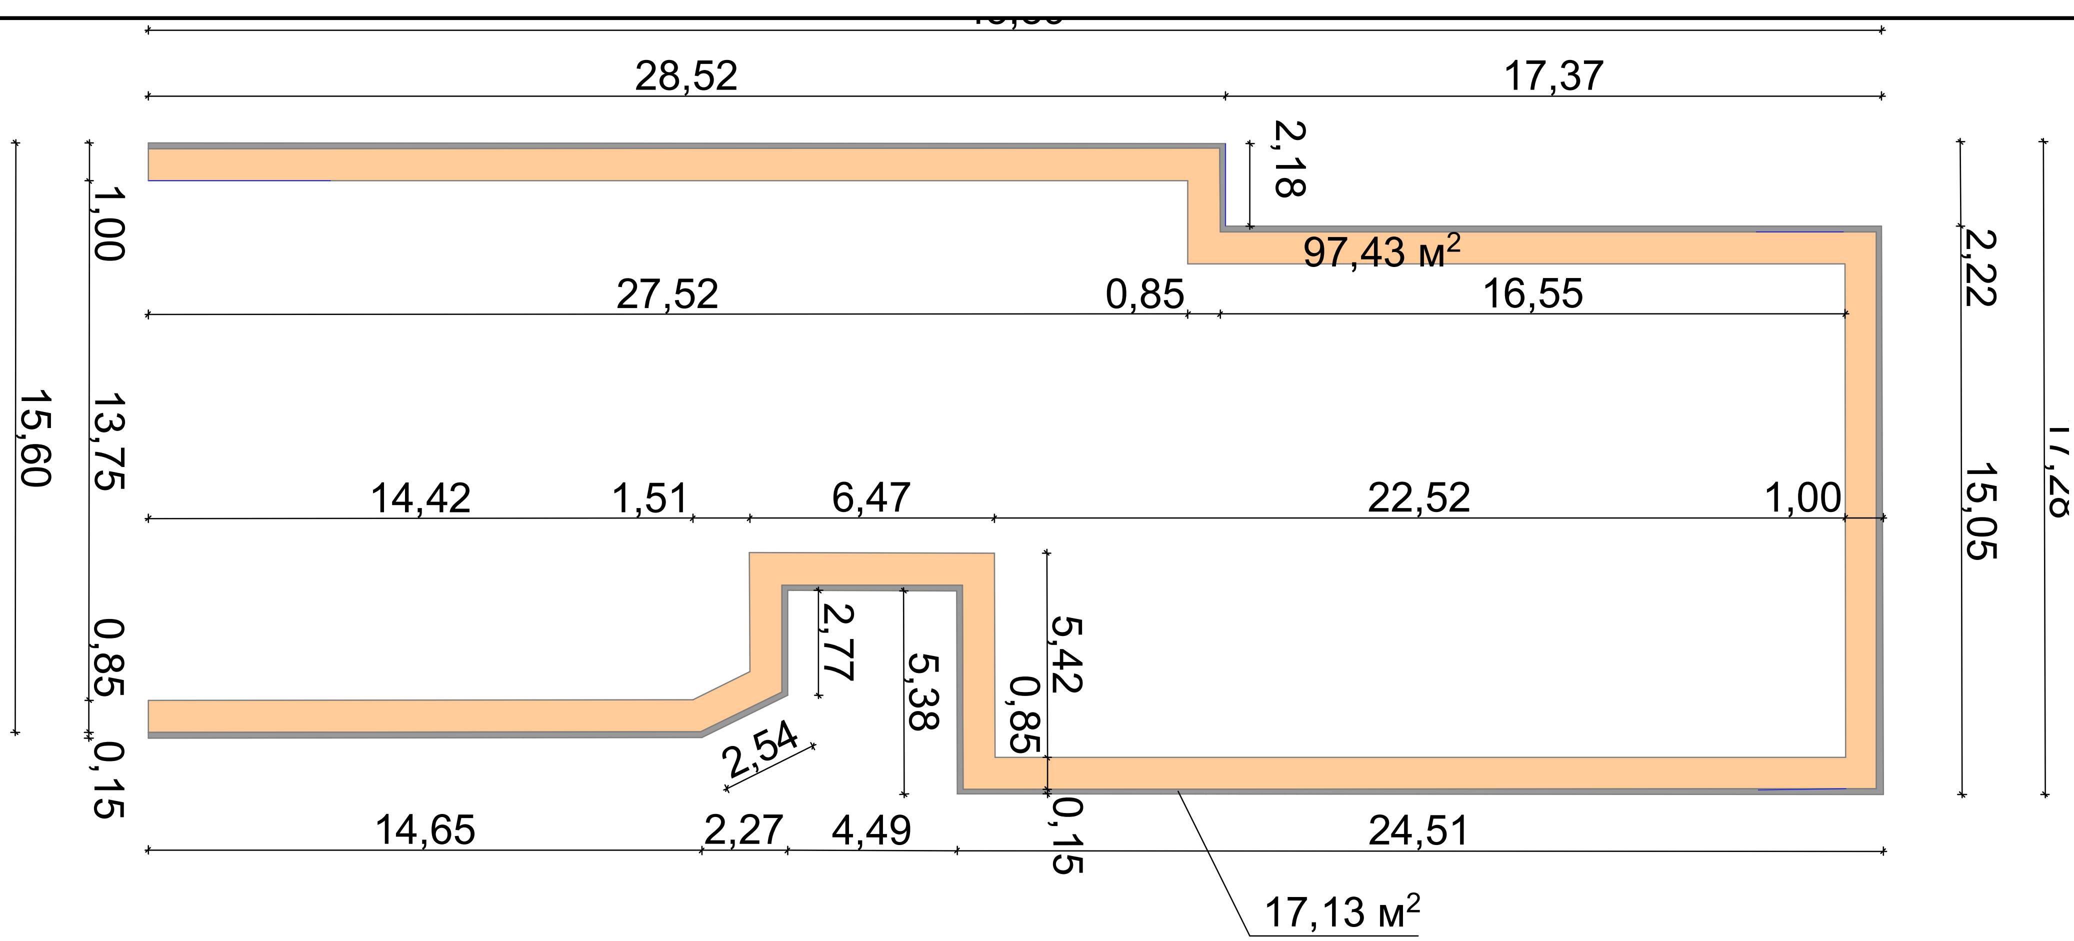

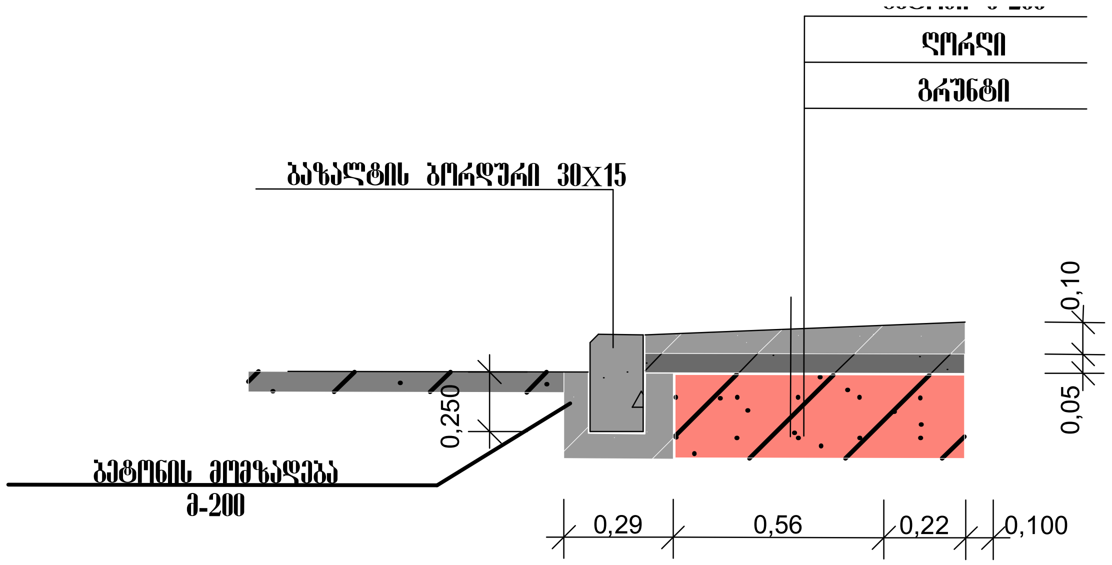

სარინელის მასალათა სპეციფიკაცია			
№	დასახელება	ზომები	მასალის ხარჯი
1	ბეტონი	97,43(მ²)X0,10	9,70 მ³
2	ბაზალტის ბორდურის ქვა	0,15(მ)X0,3(მ)X182,57 (გრძ/მ)	8,22 მ³
3	ღორღი	0,05(მ)X0,8(მ)X140,0 (მ²)	7,0 მ³

შენიშვნა:

1. შენობის მთელ პერიმეტრზე მოეწყოს ბეტონის, წყლის მოსაცილებელი სარინელი. სარინელს შემოევლოს ბაზალტის ბორდური.

KARKASI	შ.პ.ს. კარკასი			
	ობიექტი	აბასთუმნის ისტორიული ნაწილის რეკონსტრუქცია სახლი რუსთაველის ქ. № 70		
	სტადია	ესკიზური პროექტი		
დირექტორი	გ. მაჭარაშვილი		სარინელი	
არქიტექტორი	ლ. კეჩხუაშვილი		მასშტაბი	ფურცლ. რაოდენ. 15
შეასრულა	ლ. კეჩხუაშვილი		ფურცელი არ -14	2016

კარ ფანჯრები

მასშტაბი 1:50

კარ-ფანჯრების და ვიტრაჟების სპეციფიკაცია						
№	დასახ.	ზომები მ	ერთი ცალის ფართი $მ^2$	რაოდენობა ცალი	სულ ორმხრივი შესაღები ფართი $მ^2$	სულ მასალის ხარჯი მ3
1	ვი-1	2,42X2,58	6,20	4	49,60	1,24
2	ვი-2	1,66X2,58	4,30	4	34,40	0,86
3	ვი-3	1,36X2,58	3.50	2	14,00	0,35
4	ვი-4	2,42X1,83	4,43	4	35,44	0,90
5	ვი-5	1,66X1,83	3,04	4	24,32	0,61
6	ვი-6	1,36X1,83	3,80	2	15,20	0,38
7	ვი-7	2,07X1,83	3,80	3	22,80	0,57
8	ფ-1	0,90X1,80	1.62	15	48,60	1,22
9	კ-1	1,2X2,70	3,24	2	12,96	0,32
სულ ჯამში სშესაღები ფართი					257.32	6,45

კარ-ფანჯრების და ვიტრაჟების ფურნიტურის რაოდენობა	
ვიტრაჟები	62 კომპლექტი
ფანჯრები	15 კომპლექტი
კარები	2 კომპლექტი

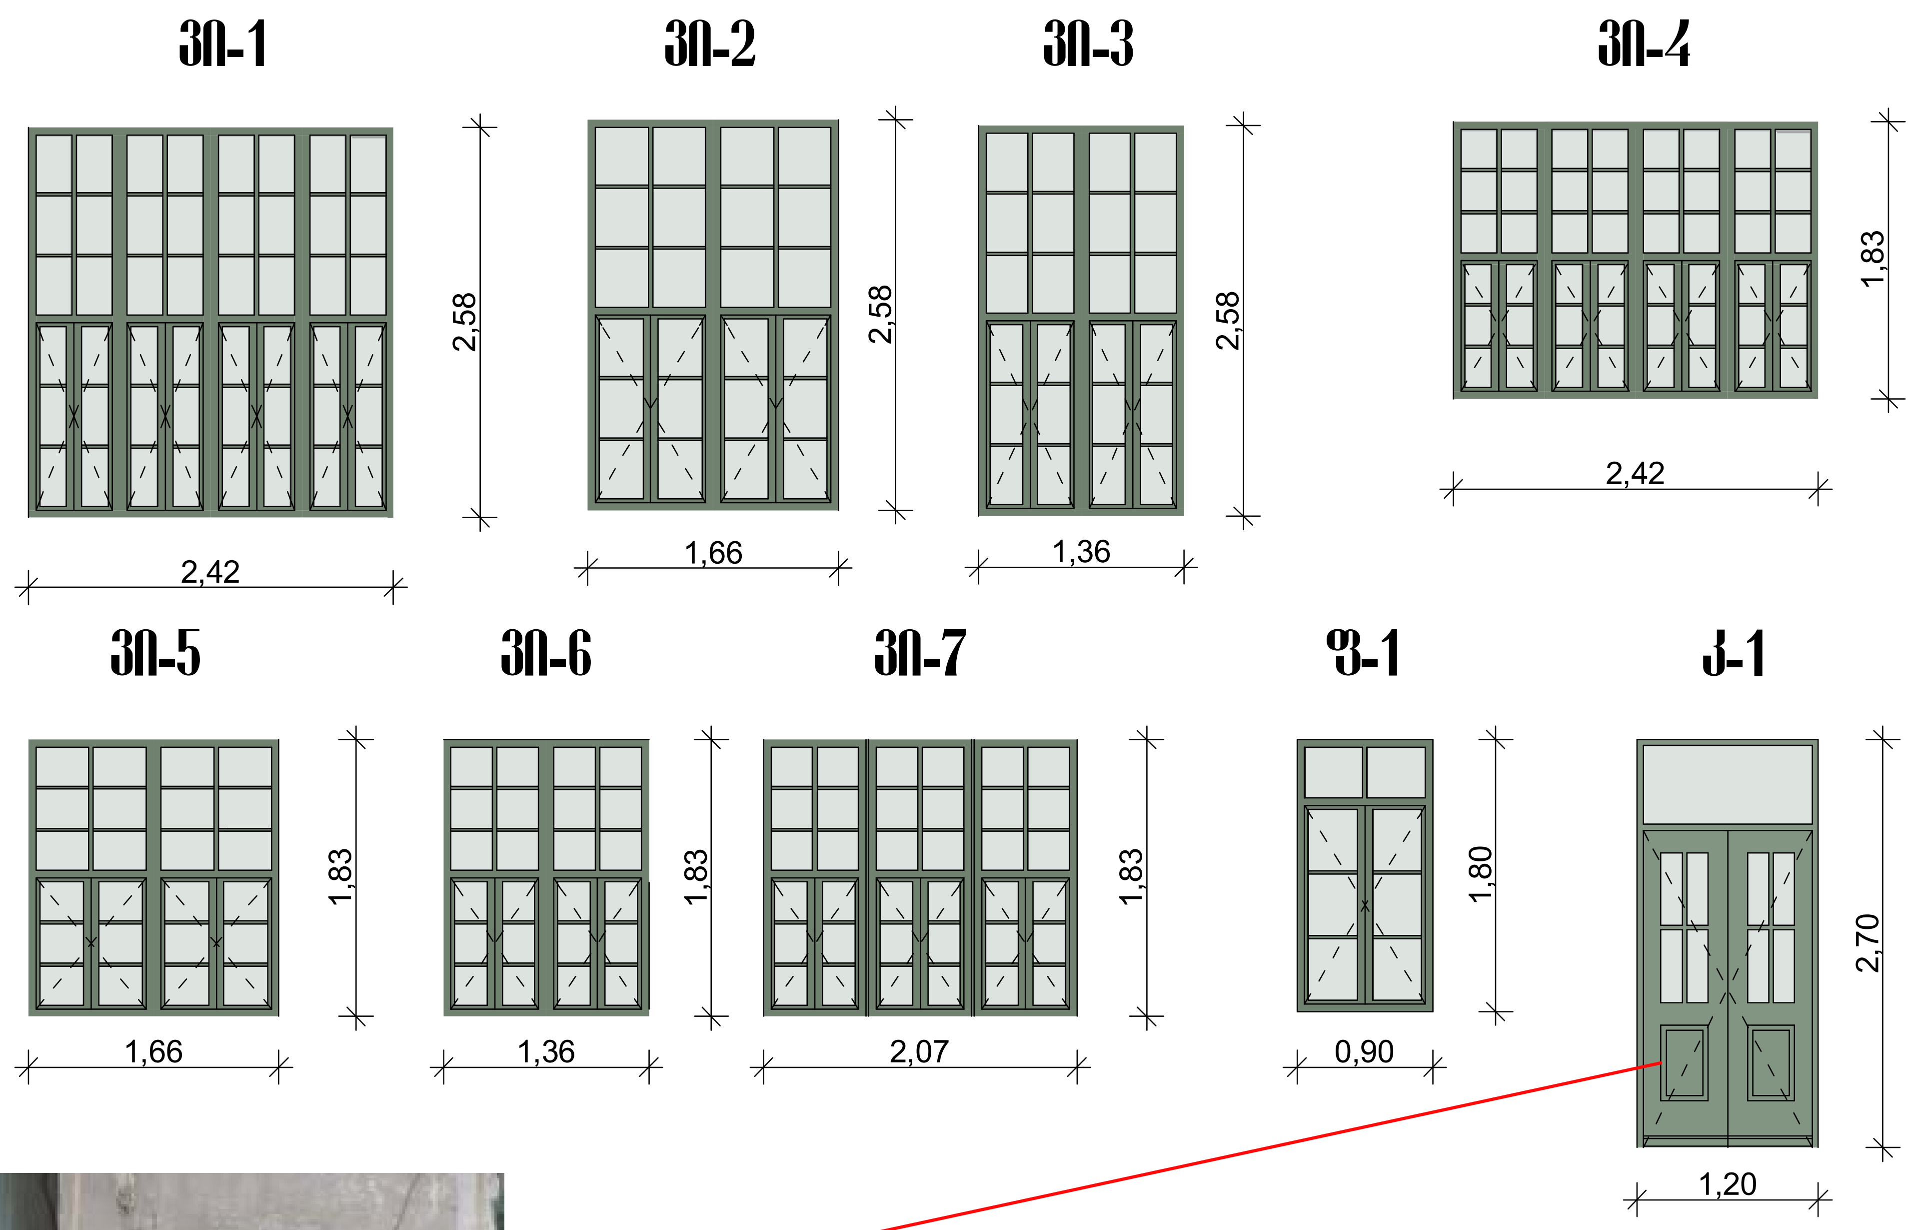

შენიშვნა:

1. არსებული საპარადე კ-1 რომელიც განთავსებულია შენობის I და II სართულებზე, პროექტის თანახმად მოიხსნას დაიშალოს დეტალებად, ჩაუტარდეს თითოეულ დეტალს სარესტავრაციო აღდგენითი სამუშაო, ანუ შეწებდეს ბზარები, დაზიანებული ფრაგმენტები ამოიჭრას და შეიცვალოს ახლით.
2. ყველა ხის დეტალის ზედაპირი დამუშავდეს და კარები აიწყოს თავიდან.
3. ორივე კარი შეიღებოს ორჯერადად ზეთოვანი საღებავით, ფერი შეთანხმდეს ავტორებთან.
4. მოხდეს არსებული ყველა ვიტრაჟის და ფანჯარა-1 ის დემონტაჟი და შეიცვალოს ახლით, ღიობებში ჩაიცვას მინაპაკეტები.
5. ყველა ახალი ვიტრაჟი და ფანჯარა-1 დამუშავდე და შეიღებოს ორჯერადად ზეთოვანი საღებავით, ფერი შეთანხმდეს ავტორებთან.

KARKASI	შ.პ.ს. კარკასი			
	ობიექტი	აბასთუმნის ისტორიული ნაწილის რეკონსტრუქცია სახლი რუსთაველის ქ. № 70		
	სტადია	ესკიზური პროექტი		
დირექტორი	გ. მაჭარაშვილი		კარ ფანჯრები	
არქიტექტორი	დ. კეჩხუაშვილი		მასშტაბი	ფურცლ. რაოდენ. 15
შეასრულა	დ. კეჩხუაშვილი		ფურცელი	არ -15 2016